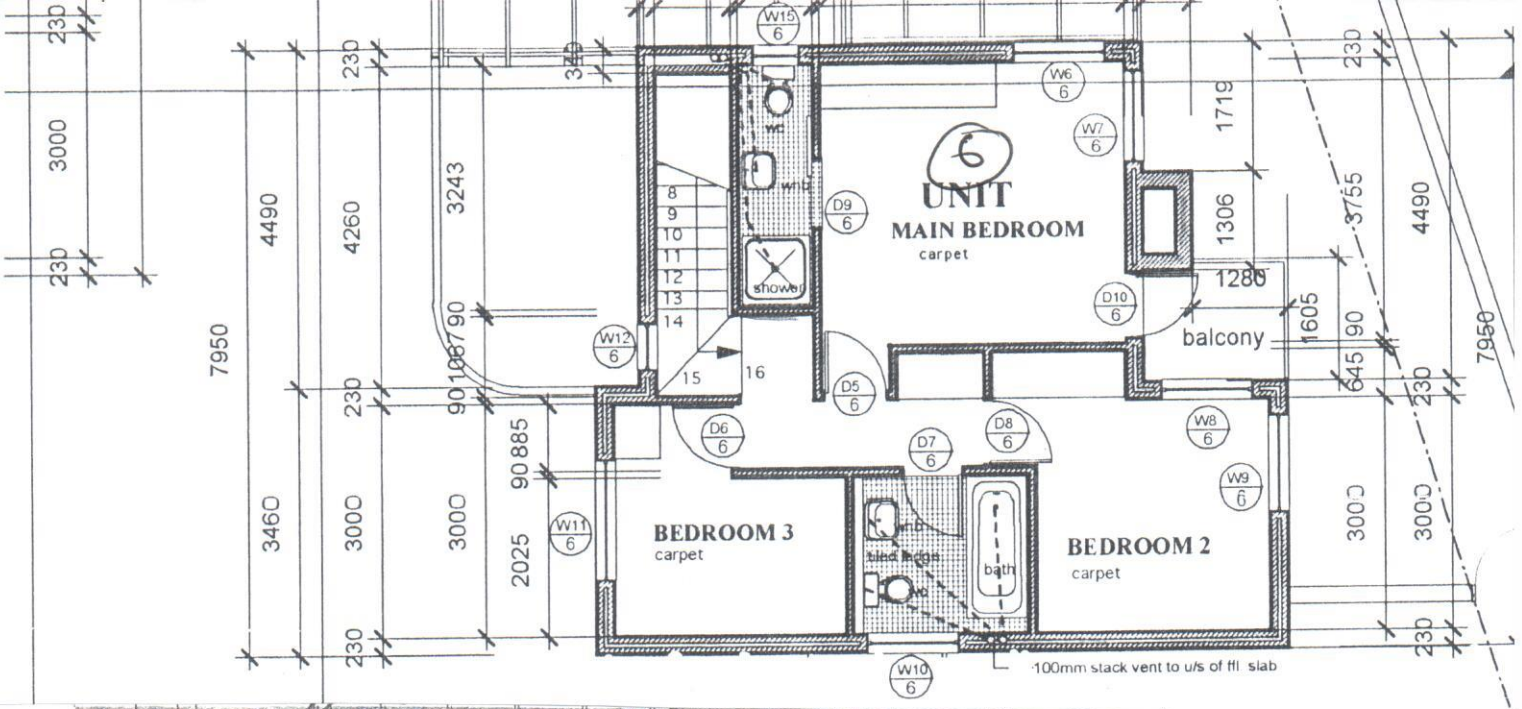
UNIT 6
MAIN BEDROOM
carpet
shower
wic
balcony
BEDROOM 3
carpet
BEDROOM 2
carpet
bath
tiled ledge
100mm stack vent to u/s of ffl slab

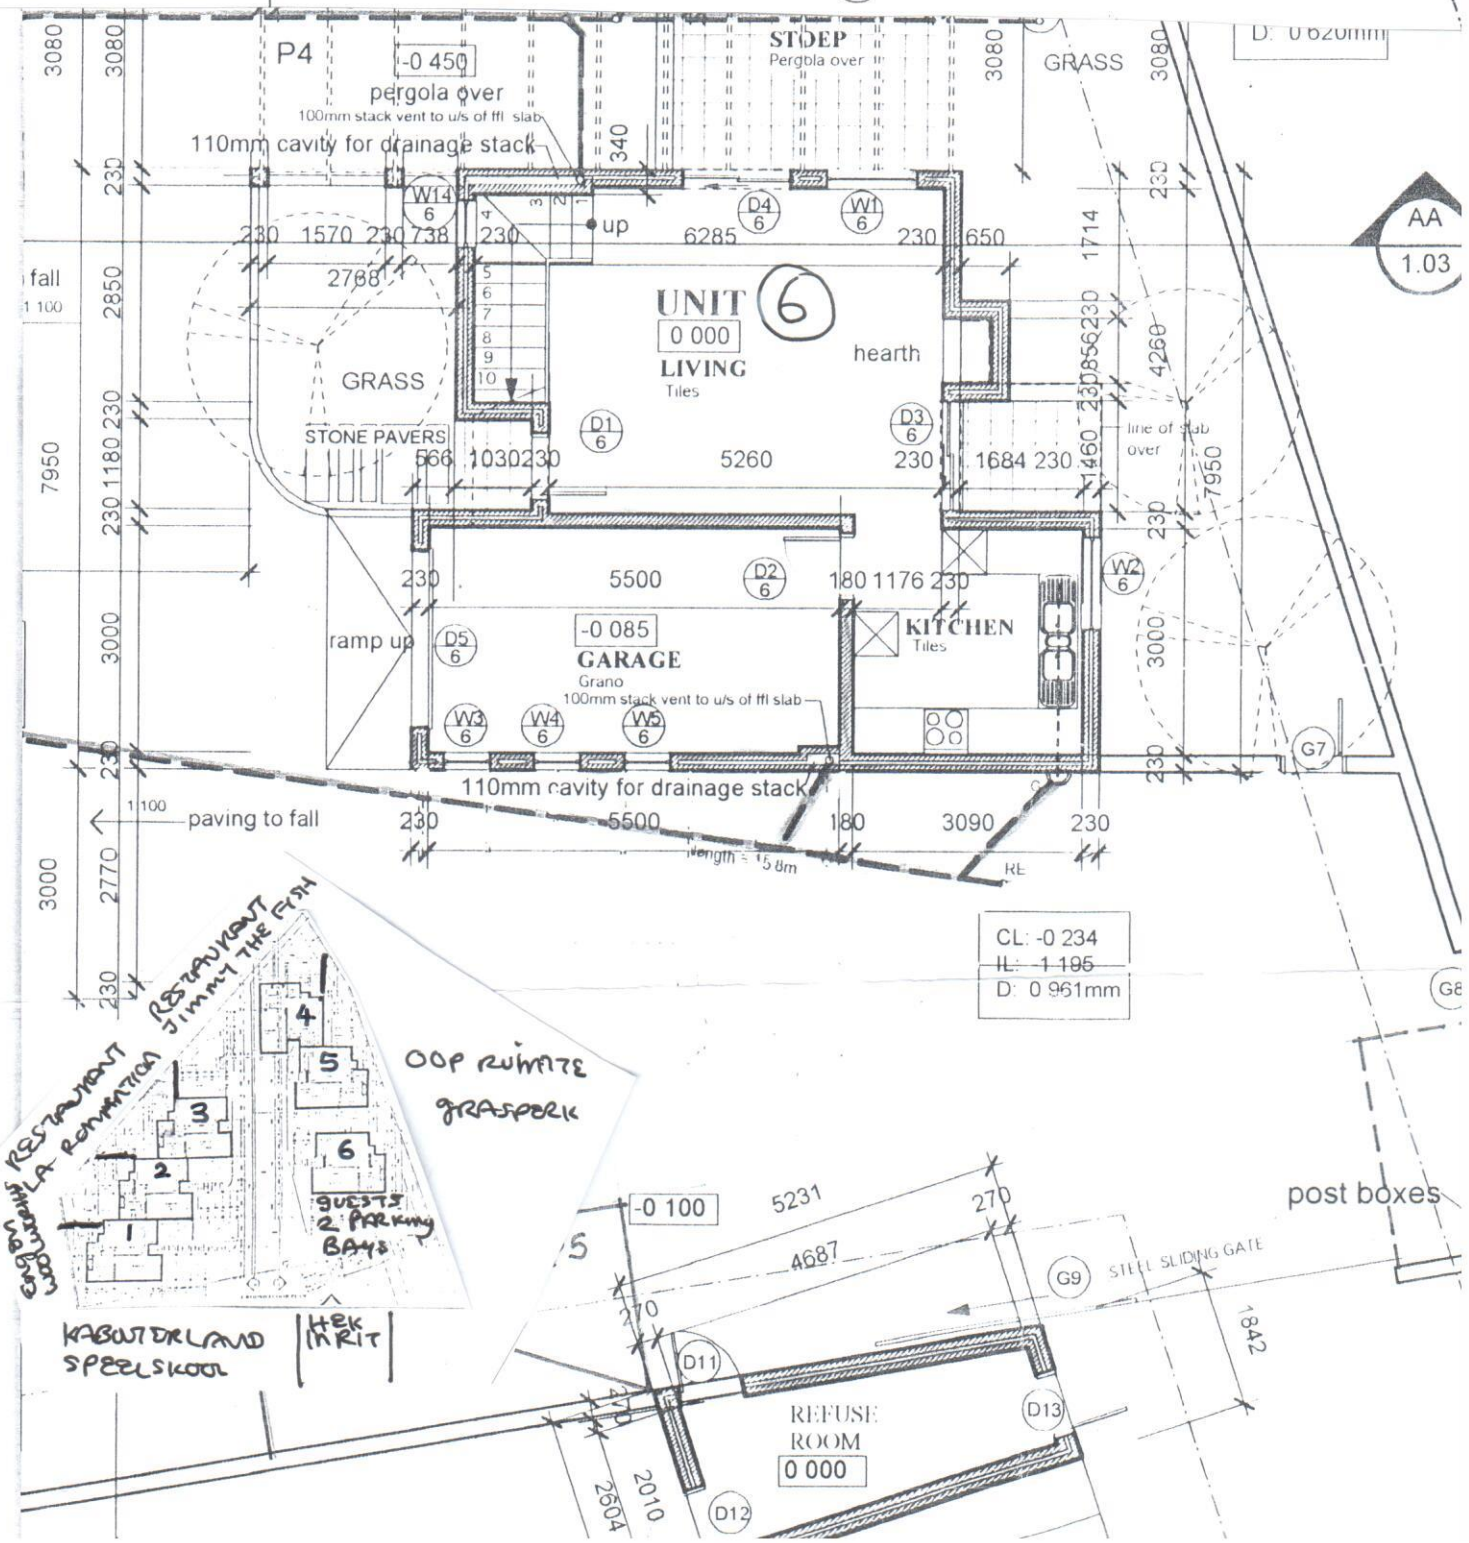
P4
-0 450
pergola over
100mm stack vent to u/s of ffl slab
110mm cavity for drainage stack
STOEP
Pergola over
GRASS
AA
1.03
UNIT 6
0 000
LIVING
Tiles
hearth
GRASS
STONE PAVERS
ramp up
-0 085
GARAGE
Grano
100mm stack vent to u/s of ffl slab
KITCHEN
Tiles
110mm cavity for drainage stack
paving to fall
CL: -0 234
IL: -1 195
D: 0 961mm
post boxes
-0 100
STEEL SLIDING GATE
REFUSE ROOM
0 000